


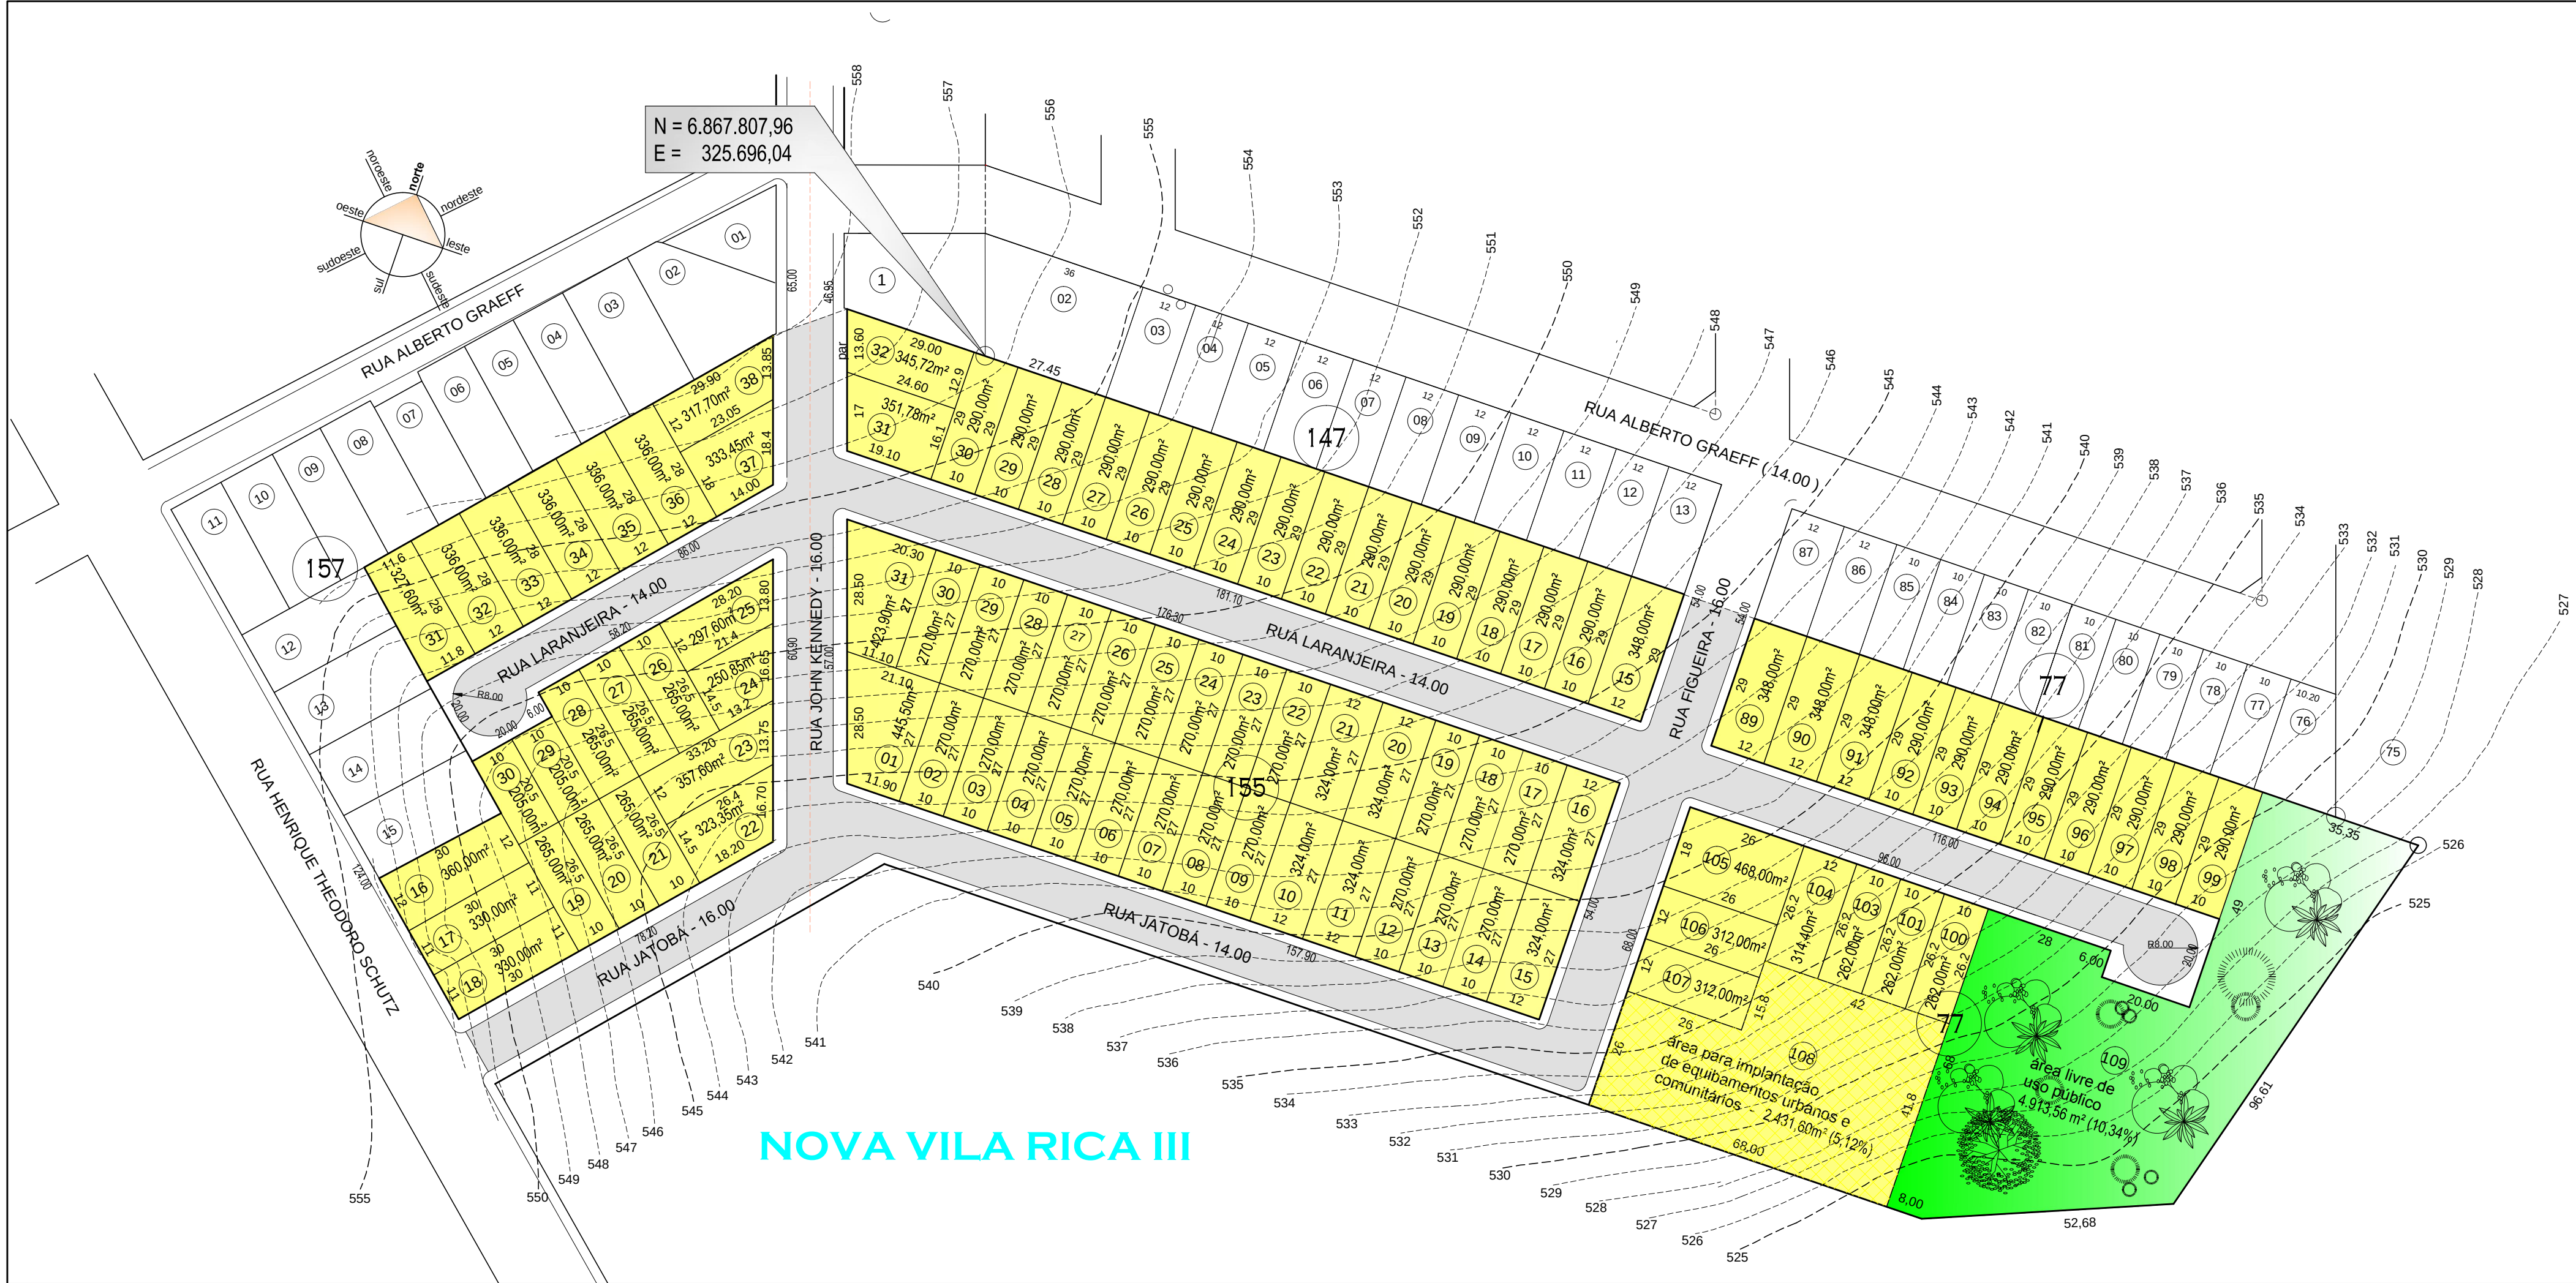

DIRETRIZES (conforme protocolo 11515/2022 - 13/12/2022)				
1 -	A presente documentação, PROJETO URBANÍSTICO, para aprovação em PRIMEIRA FASE segue a Lei Complementar 218/2018 e suas alterações;			
2 -	A localização e dimensionamento do sistema viário, as áreas destinadas a equipamentos urbanos e comunitários e dos espaços livres de uso público seguem a prancha 02/04, vistas;			
3 -	As áreas de espaços livres de uso público e a de equipamentos urbanos e comunitários foram aceitas conforme prancha 02/04 pelo prefeito Sr. Milton Schmitz;			
4 -	O EIV - estudo de impacto de vizinhança, foi elaborado e analisado conforme PARECER TÉCNICO CONCLUSIVO DE EIV Nº 01/2023;			
5 -	Anexo informação cadastral com número das quadras e lotes.			

SERGIO KIRINUS IMÓVEIS - EIRELI - CNPJ 20.221.664/0001-98

CRISTIAN KIRINUS IMÓVEIS - EIRELI - CNPJ 19.915.816/0001-73

06.	20/04/2023	PARECER TÉCNICO CONCLUSIVO DE EIV Nº 01/2023	planej.	
05.	outubro/22	EIV - estudo de impacto de vizinhança	geron	
04.	29/03/23	implantação das ruas e lotes	geron	
03.	12/09/22	alteração área livre + APP	geron	
02.	09/12/21	alteração área livre + rua Laranjeira + rua John Kennedy	geron	
01.	07/04/21	projeto urbanístico	geron	
rev.	data	descrição	elab.	aprov.

PARCELAMENTO DO SOLO

NOVA VILA RICA III

SERGIO GILBERTO KIRINUS

eng. civil crea 18.973

proprietário

SERGIO KIRINUS IMÓVEIS - EIRELI

CRISTIAN KIRINUS IMÓVEIS - EIRELI

local

RUA HENRIQUE THEODORO SCHUTZ - VILA RICA - CARAZINHO (RS)

projeto e execução

matrícula:

45.147 - Lº 2 RG

objeto

URBANISMO

PLANTA GERAL DOS LOTES

setor

007

quadra

147

lote

014

área

47.522,17 m²

escala

1:1000

data

set/2022